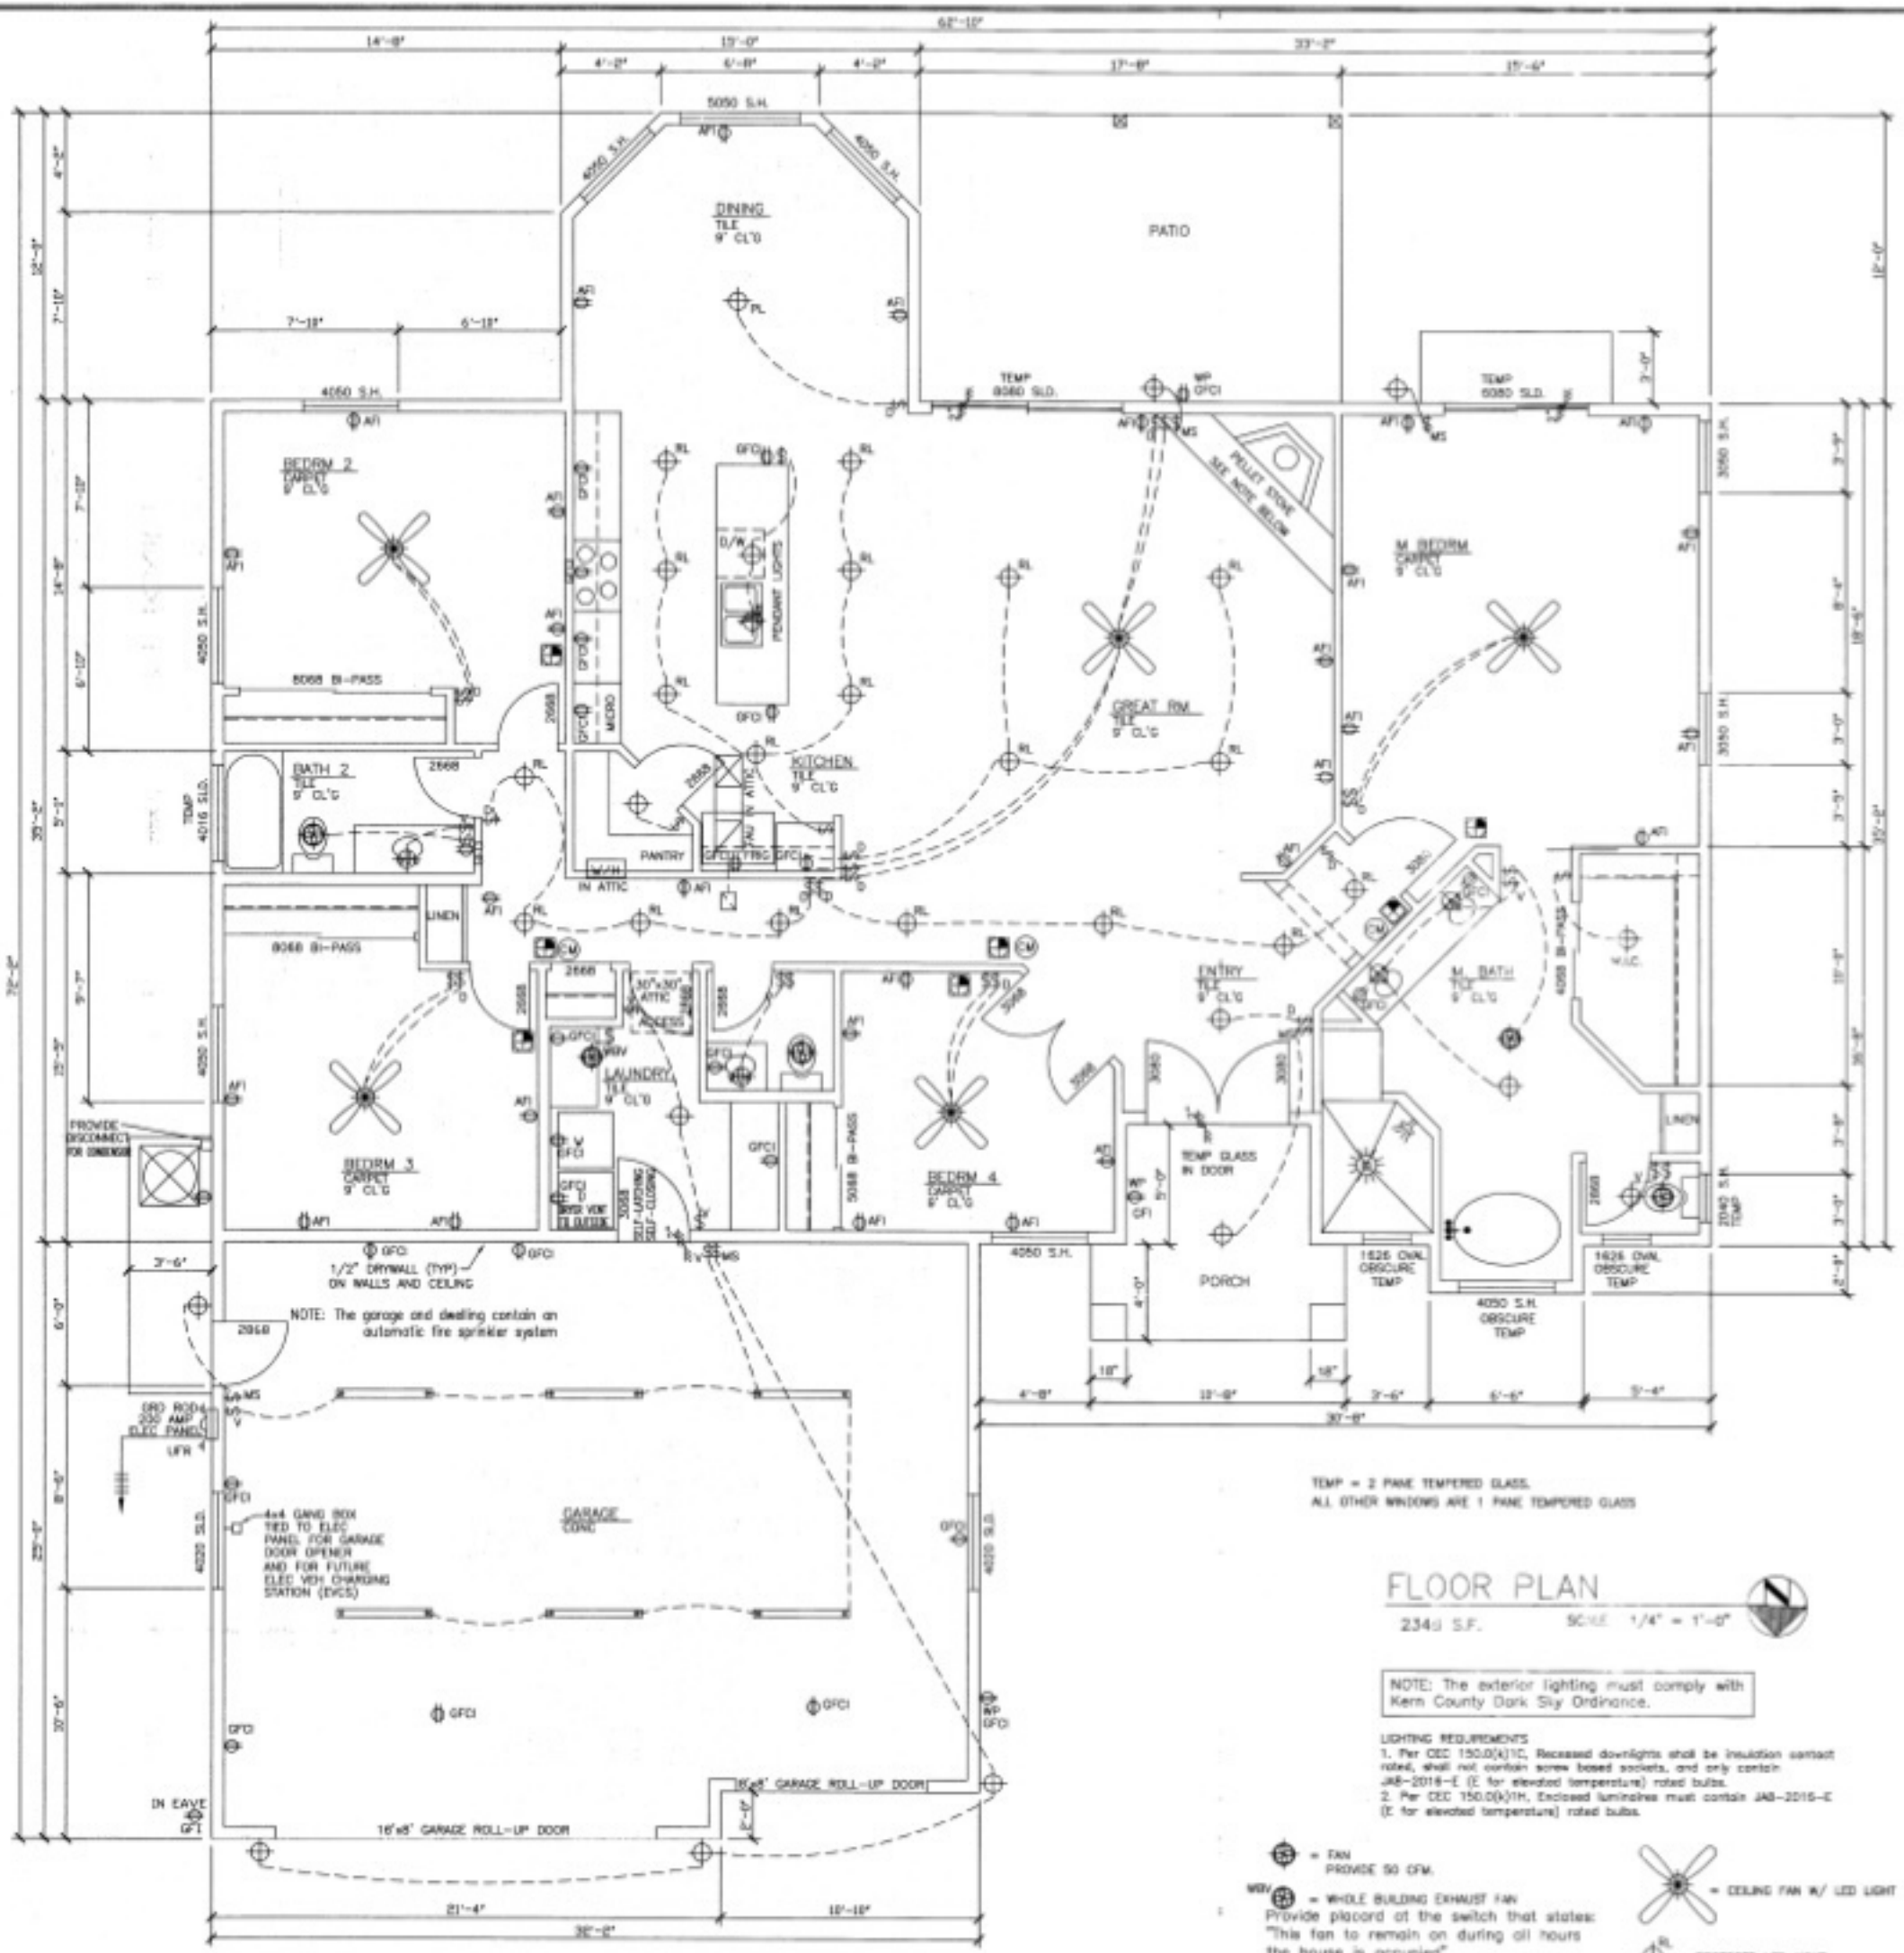


TEMP = 2 PANE TEMPERED GLASS.
ALL OTHER WINDOWS ARE 1 PANE TEMPERED GLASS

FLOOR PLAN

2340 S.F. SCALE 1/4" = 1'-0"

NOTE: The exterior lighting must comply with Kern County Dark Sky Ordinance.

LIGHTING REQUIREMENTS
1. Per CEC 150.0(k)1C, Recessed downlights shall be insulation contact rated, shall not contain screw based sockets, and only contain JA8-2016-E (E for elevated temperature) rated bulbs.
2. Per CEC 150.0(k)1H, Enclosed luminaires must contain JA8-2016-E (E for elevated temperature) rated bulbs.

= FAN PROVIDE 50 CFM.

WBV = WHOLE BUILDING EXHAUST FAN
Provide placard at the switch that states: "This fan to remain on during all hours the house is occupied"

= CEILING FAN W/ LED LIGHT

= RECESSED LED LIGHT

= CONVENIENCE OUTLET DUPLEX