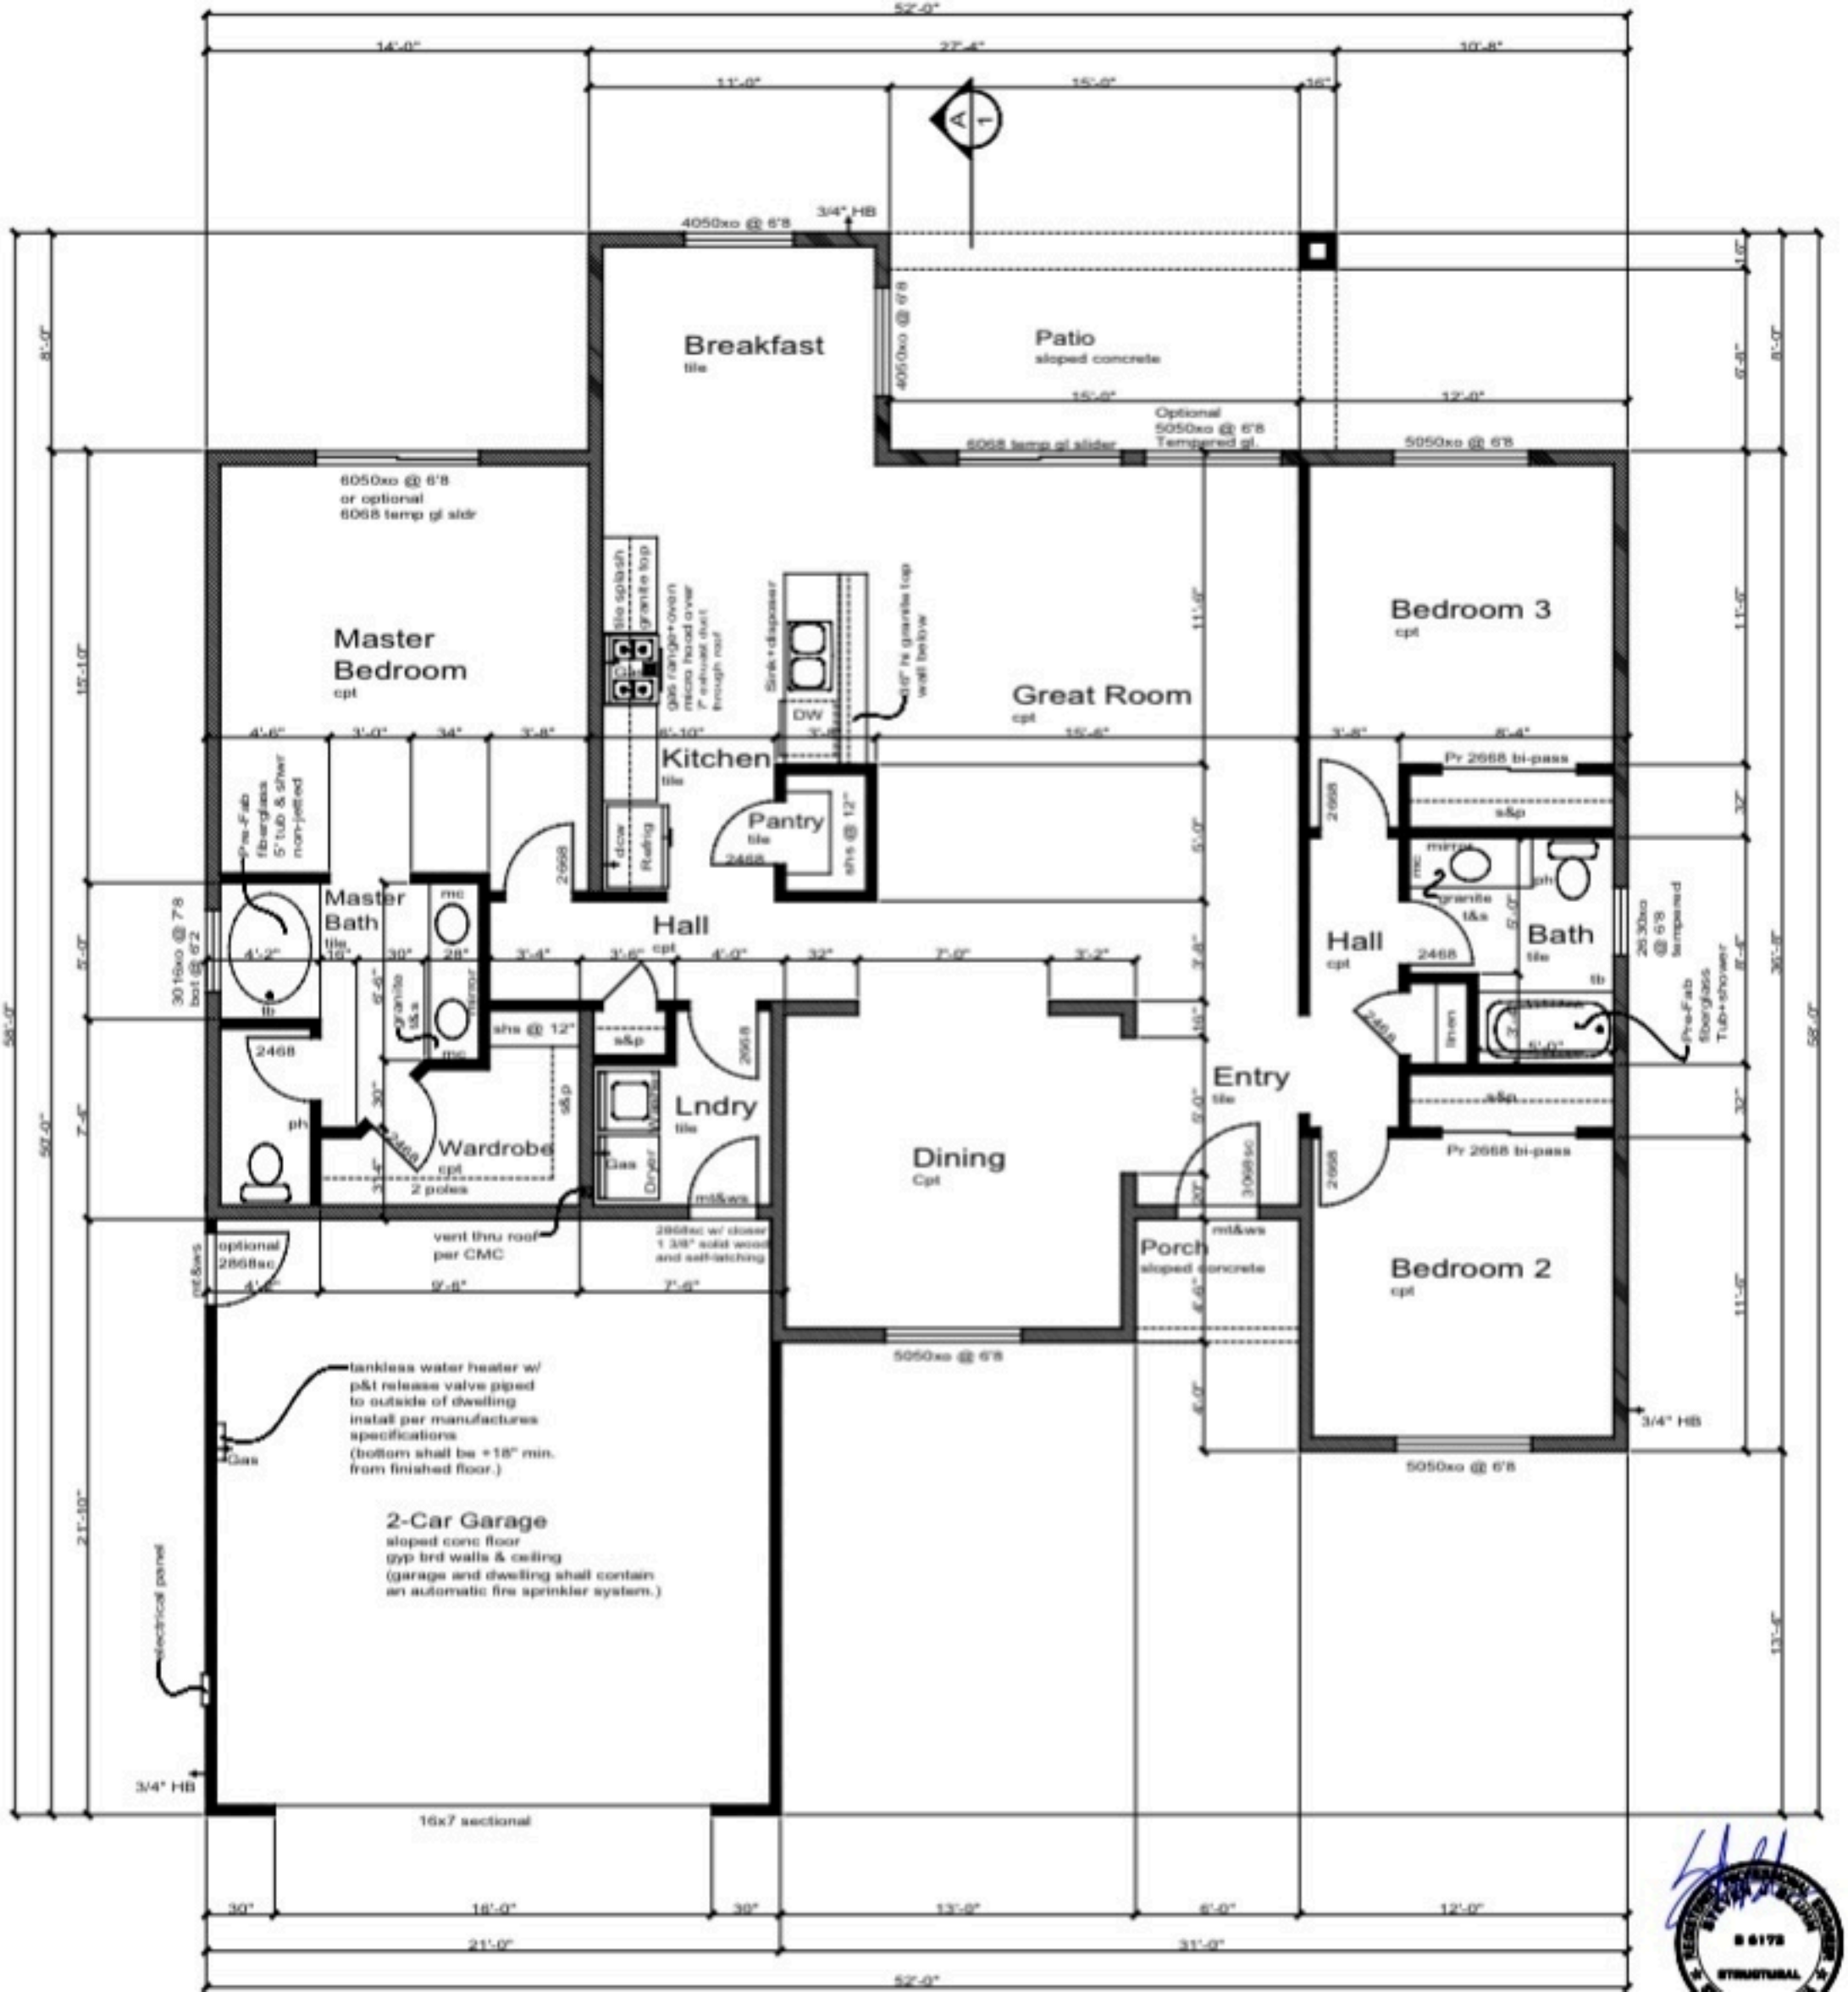

52'-0"
14'-0"
27'-4"
10'-8"
11'-0"
15'-0"
16"
A 1
4050xo @ 6'8
3/4" HB
Breakfast
tile
4050xo @ 6'8
Patio
sloped concrete
15'-0"
12'-0"
Optional
5050xo @ 6'8
Tempered gl.
6068 temp gl slider
5050xo @ 6'8
6050xo @ 6'8
or optional
6068 temp gl sldr
Master
Bedroom
cpt
tile splash
granite top
gas range+oven
micro hood over
7" exhaust duct
through roof
Sink+disposer
DW
6'0" hi granite top
wall below
Great Room
cpt
Bedroom 3
cpt
Kitchen
tile
Pantry
tile
2468
shs @ 12"
dcw
Refrig
2668
Pr 2668 bi-pass
s&p
mc
mirror
granite
t&s
Pre-Fab
fiberglass
5' tub & shwr
non-jetted
Master
Bath
tile
Hall
cpt
Hall
cpt
2468
Bath
tile
tb
Pre-Fab
fiberglass
Tub+shower
2630xo
@ 6'8
tempered
linen
ph
Wardrobe
cpt
2 poles
shs @ 12"
s&p
Lndry
tile
Washer
Dryer
Gas
2668
Entry
tile
Dining
Cpt
Porch
sloped concrete
mt&ws
optional
2868sc
vent thru roof
per CMC
2868sc w/ closer
1 3/8" solid wood
and self-latching
Bedroom 2
cpt
5050xo @ 6'8
3/4" HB
tankless water heater w/
p&t release valve piped
to outside of dwelling
install per manufactures
specifications
(bottom shall be +18" min.
from finished floor.)
Gas
2-Car Garage
sloped conc floor
gyp brd walls & ceiling
(garage and dwelling shall contain
an automatic fire sprinkler system.)
electrical panel
3/4" HB
16x7 sectional
30"
16'-0"
30"
13'-0"
6'-0"
12'-0"
21'-0"
31'-0"
52'-0"